

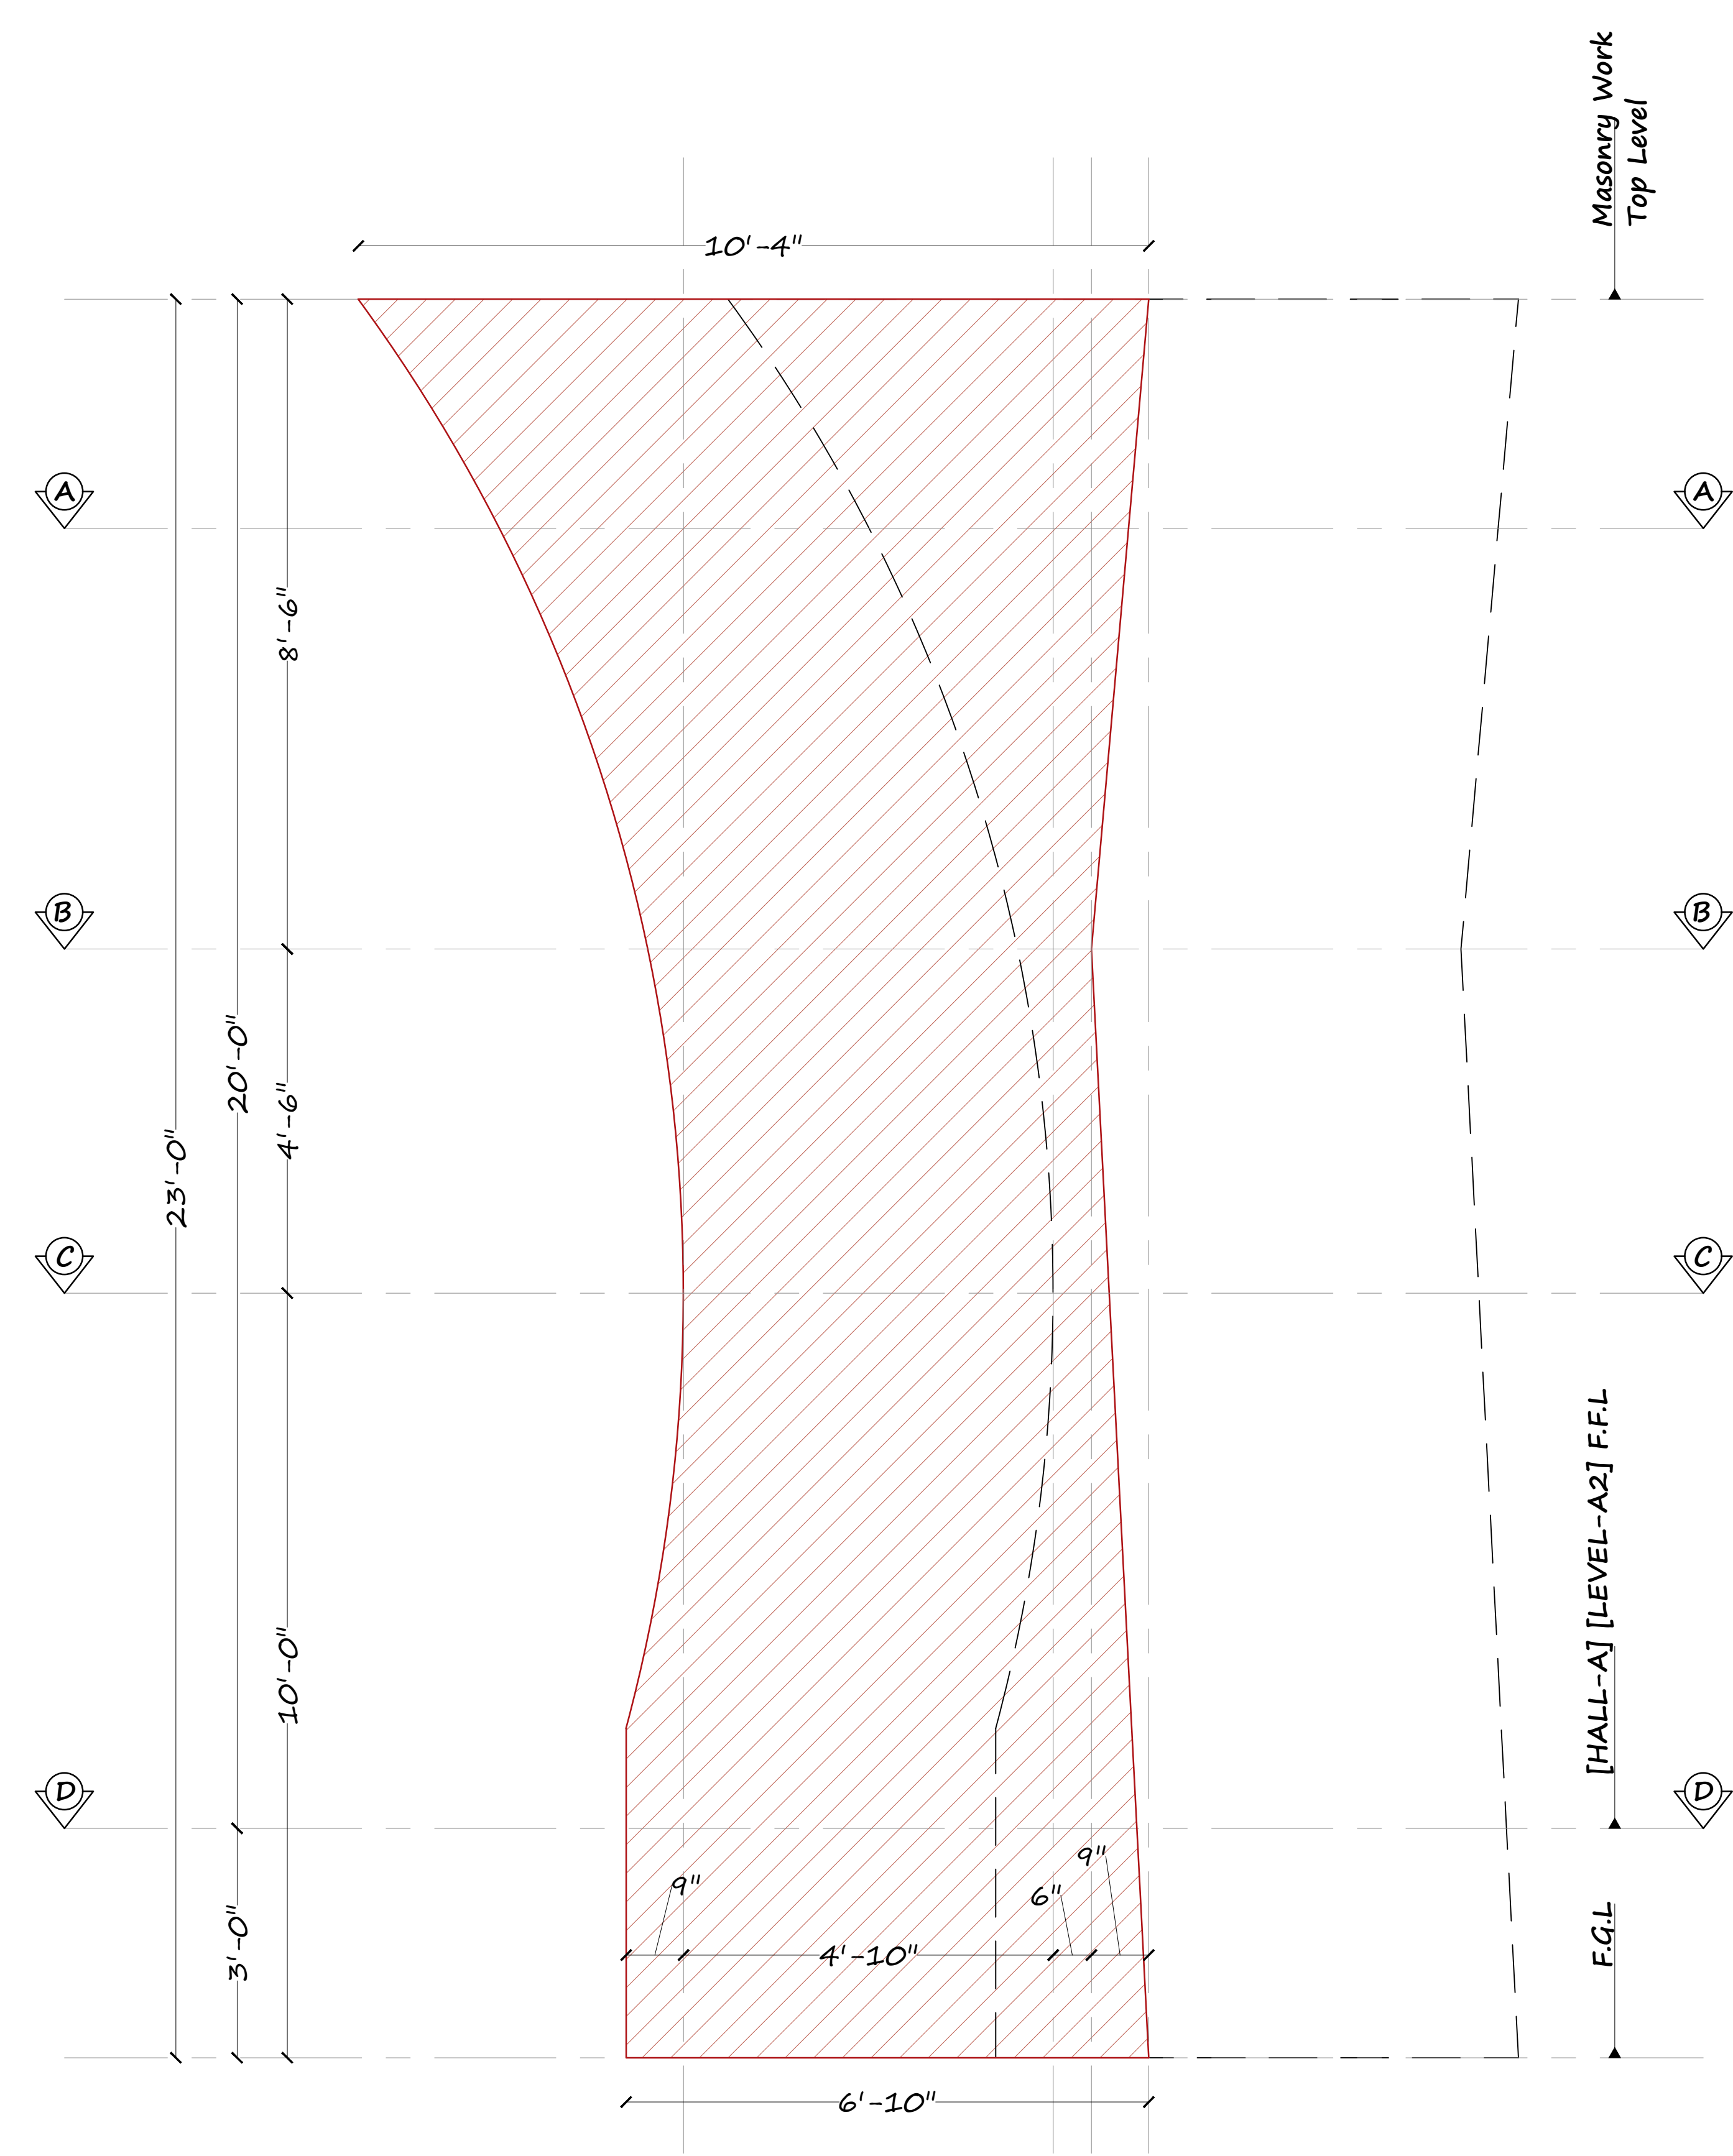


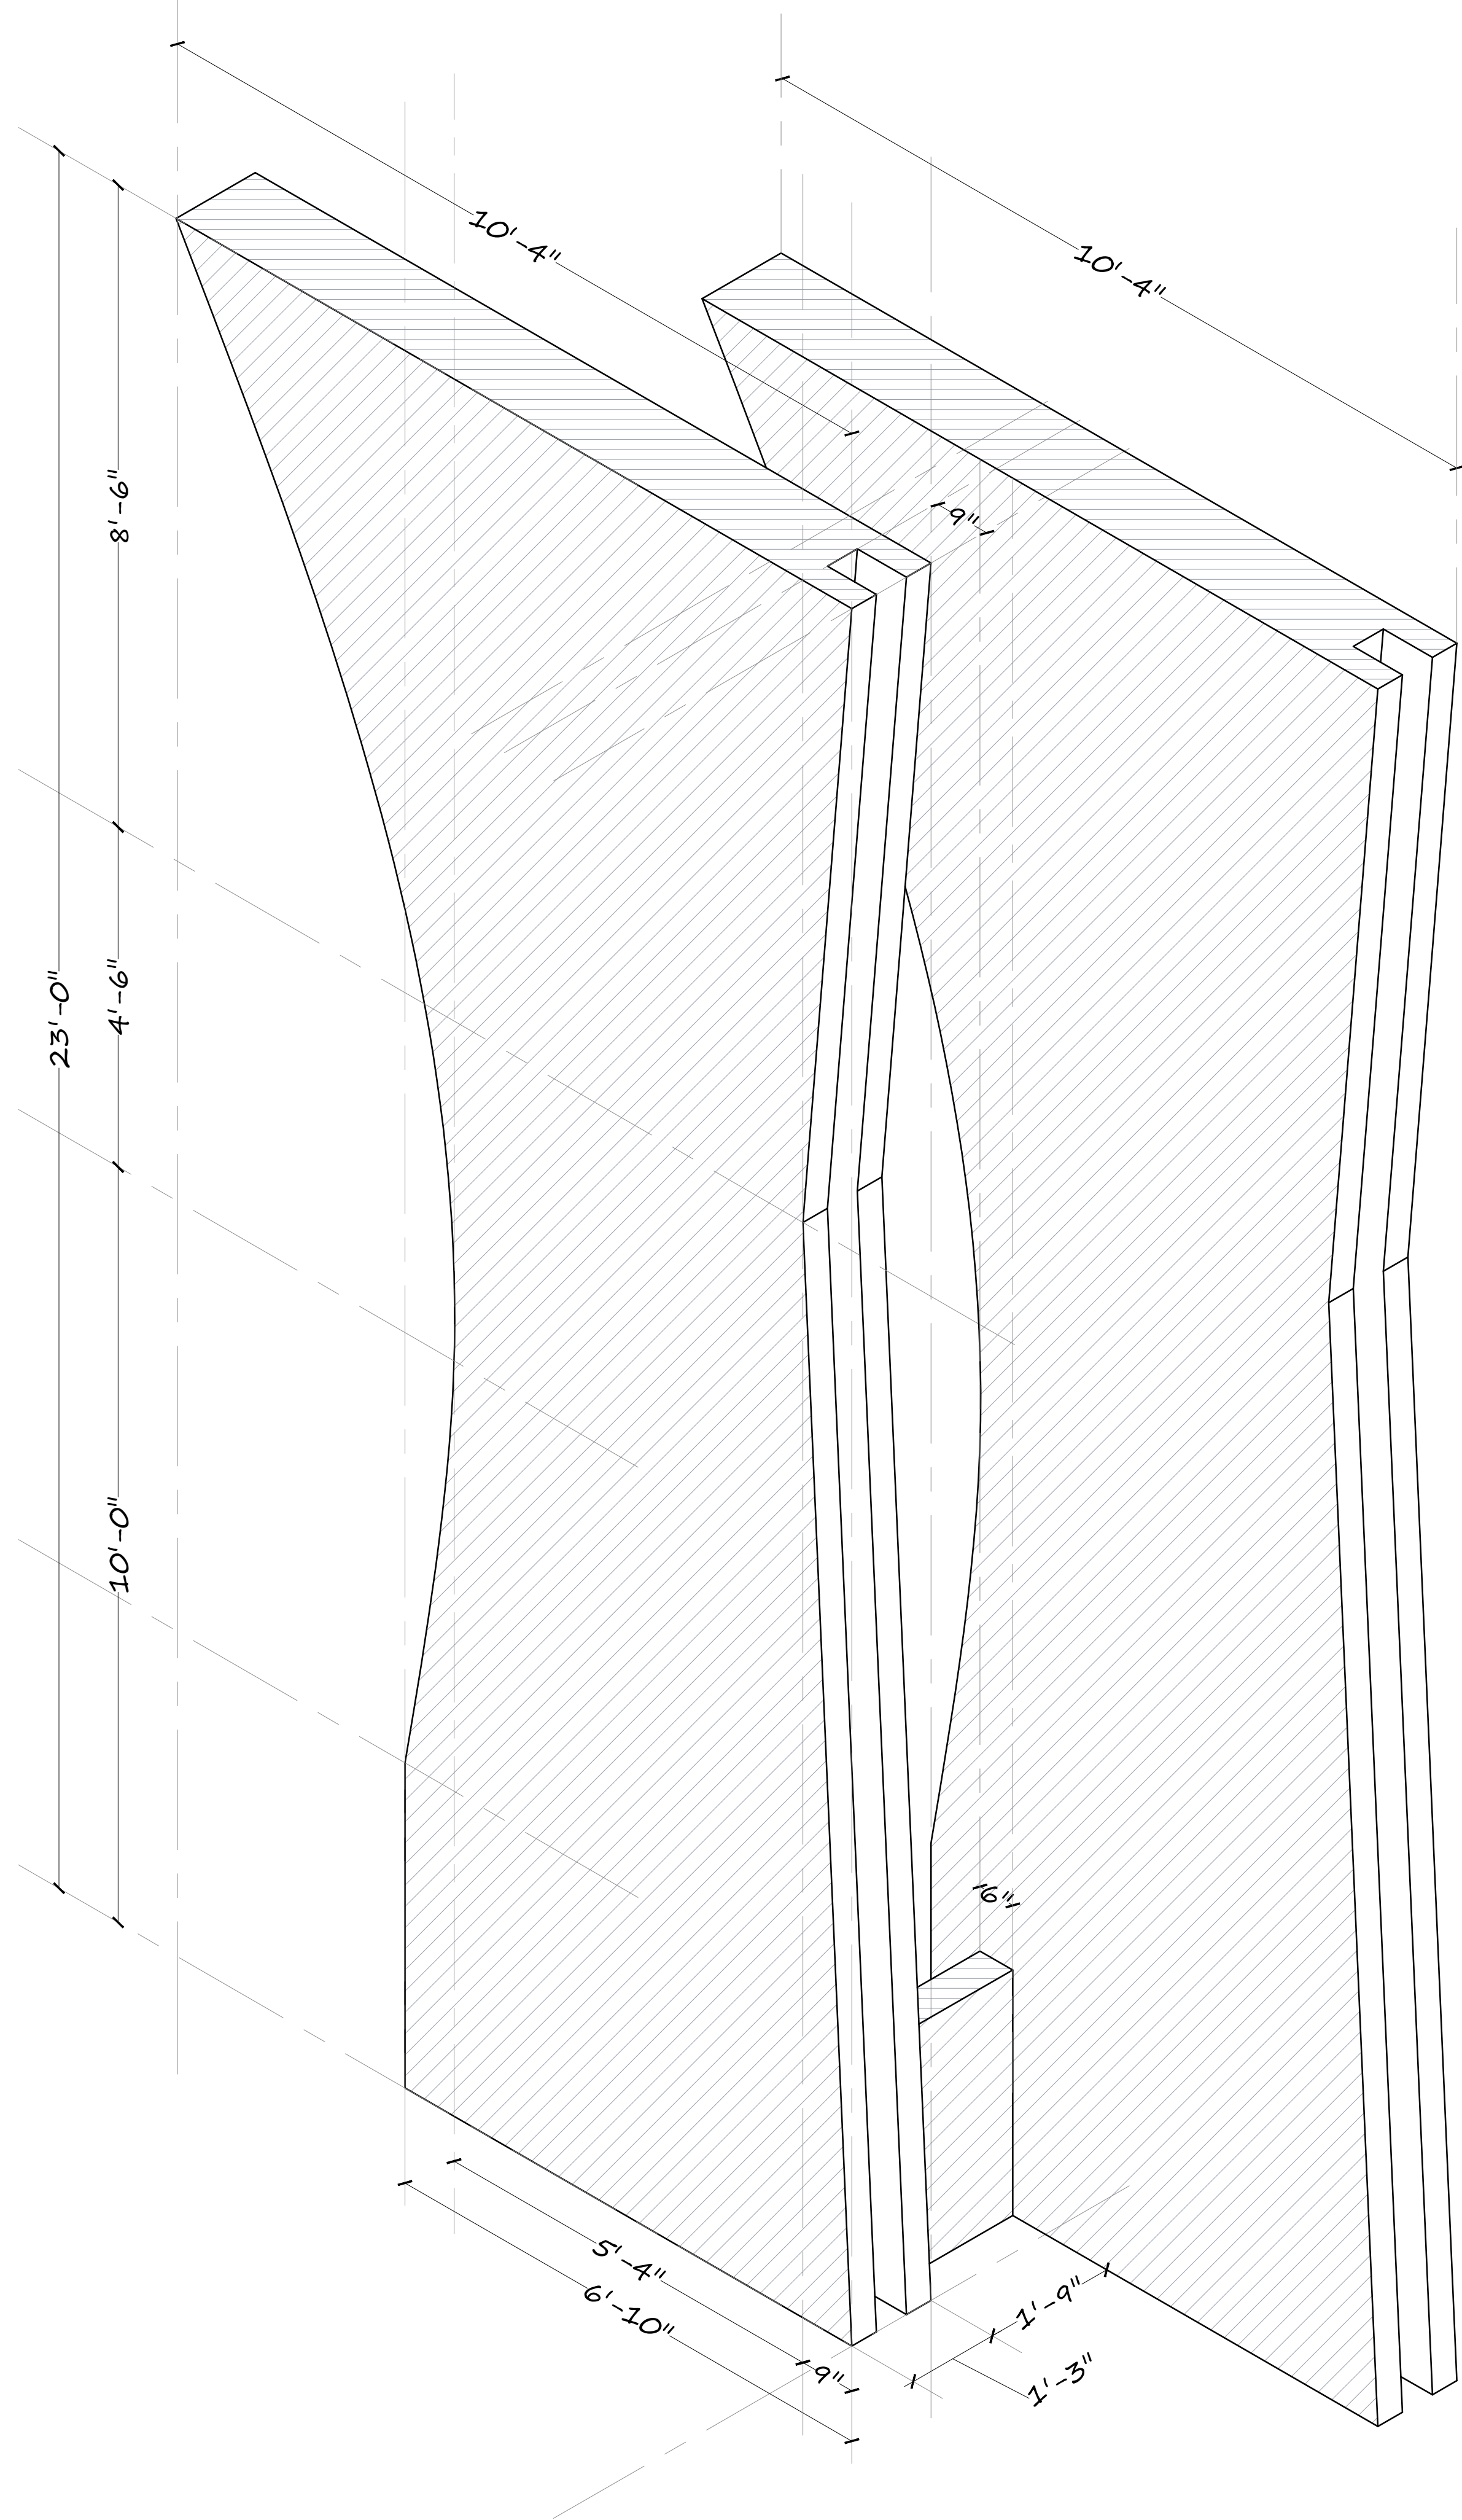

SECTIONAL ELEVATION

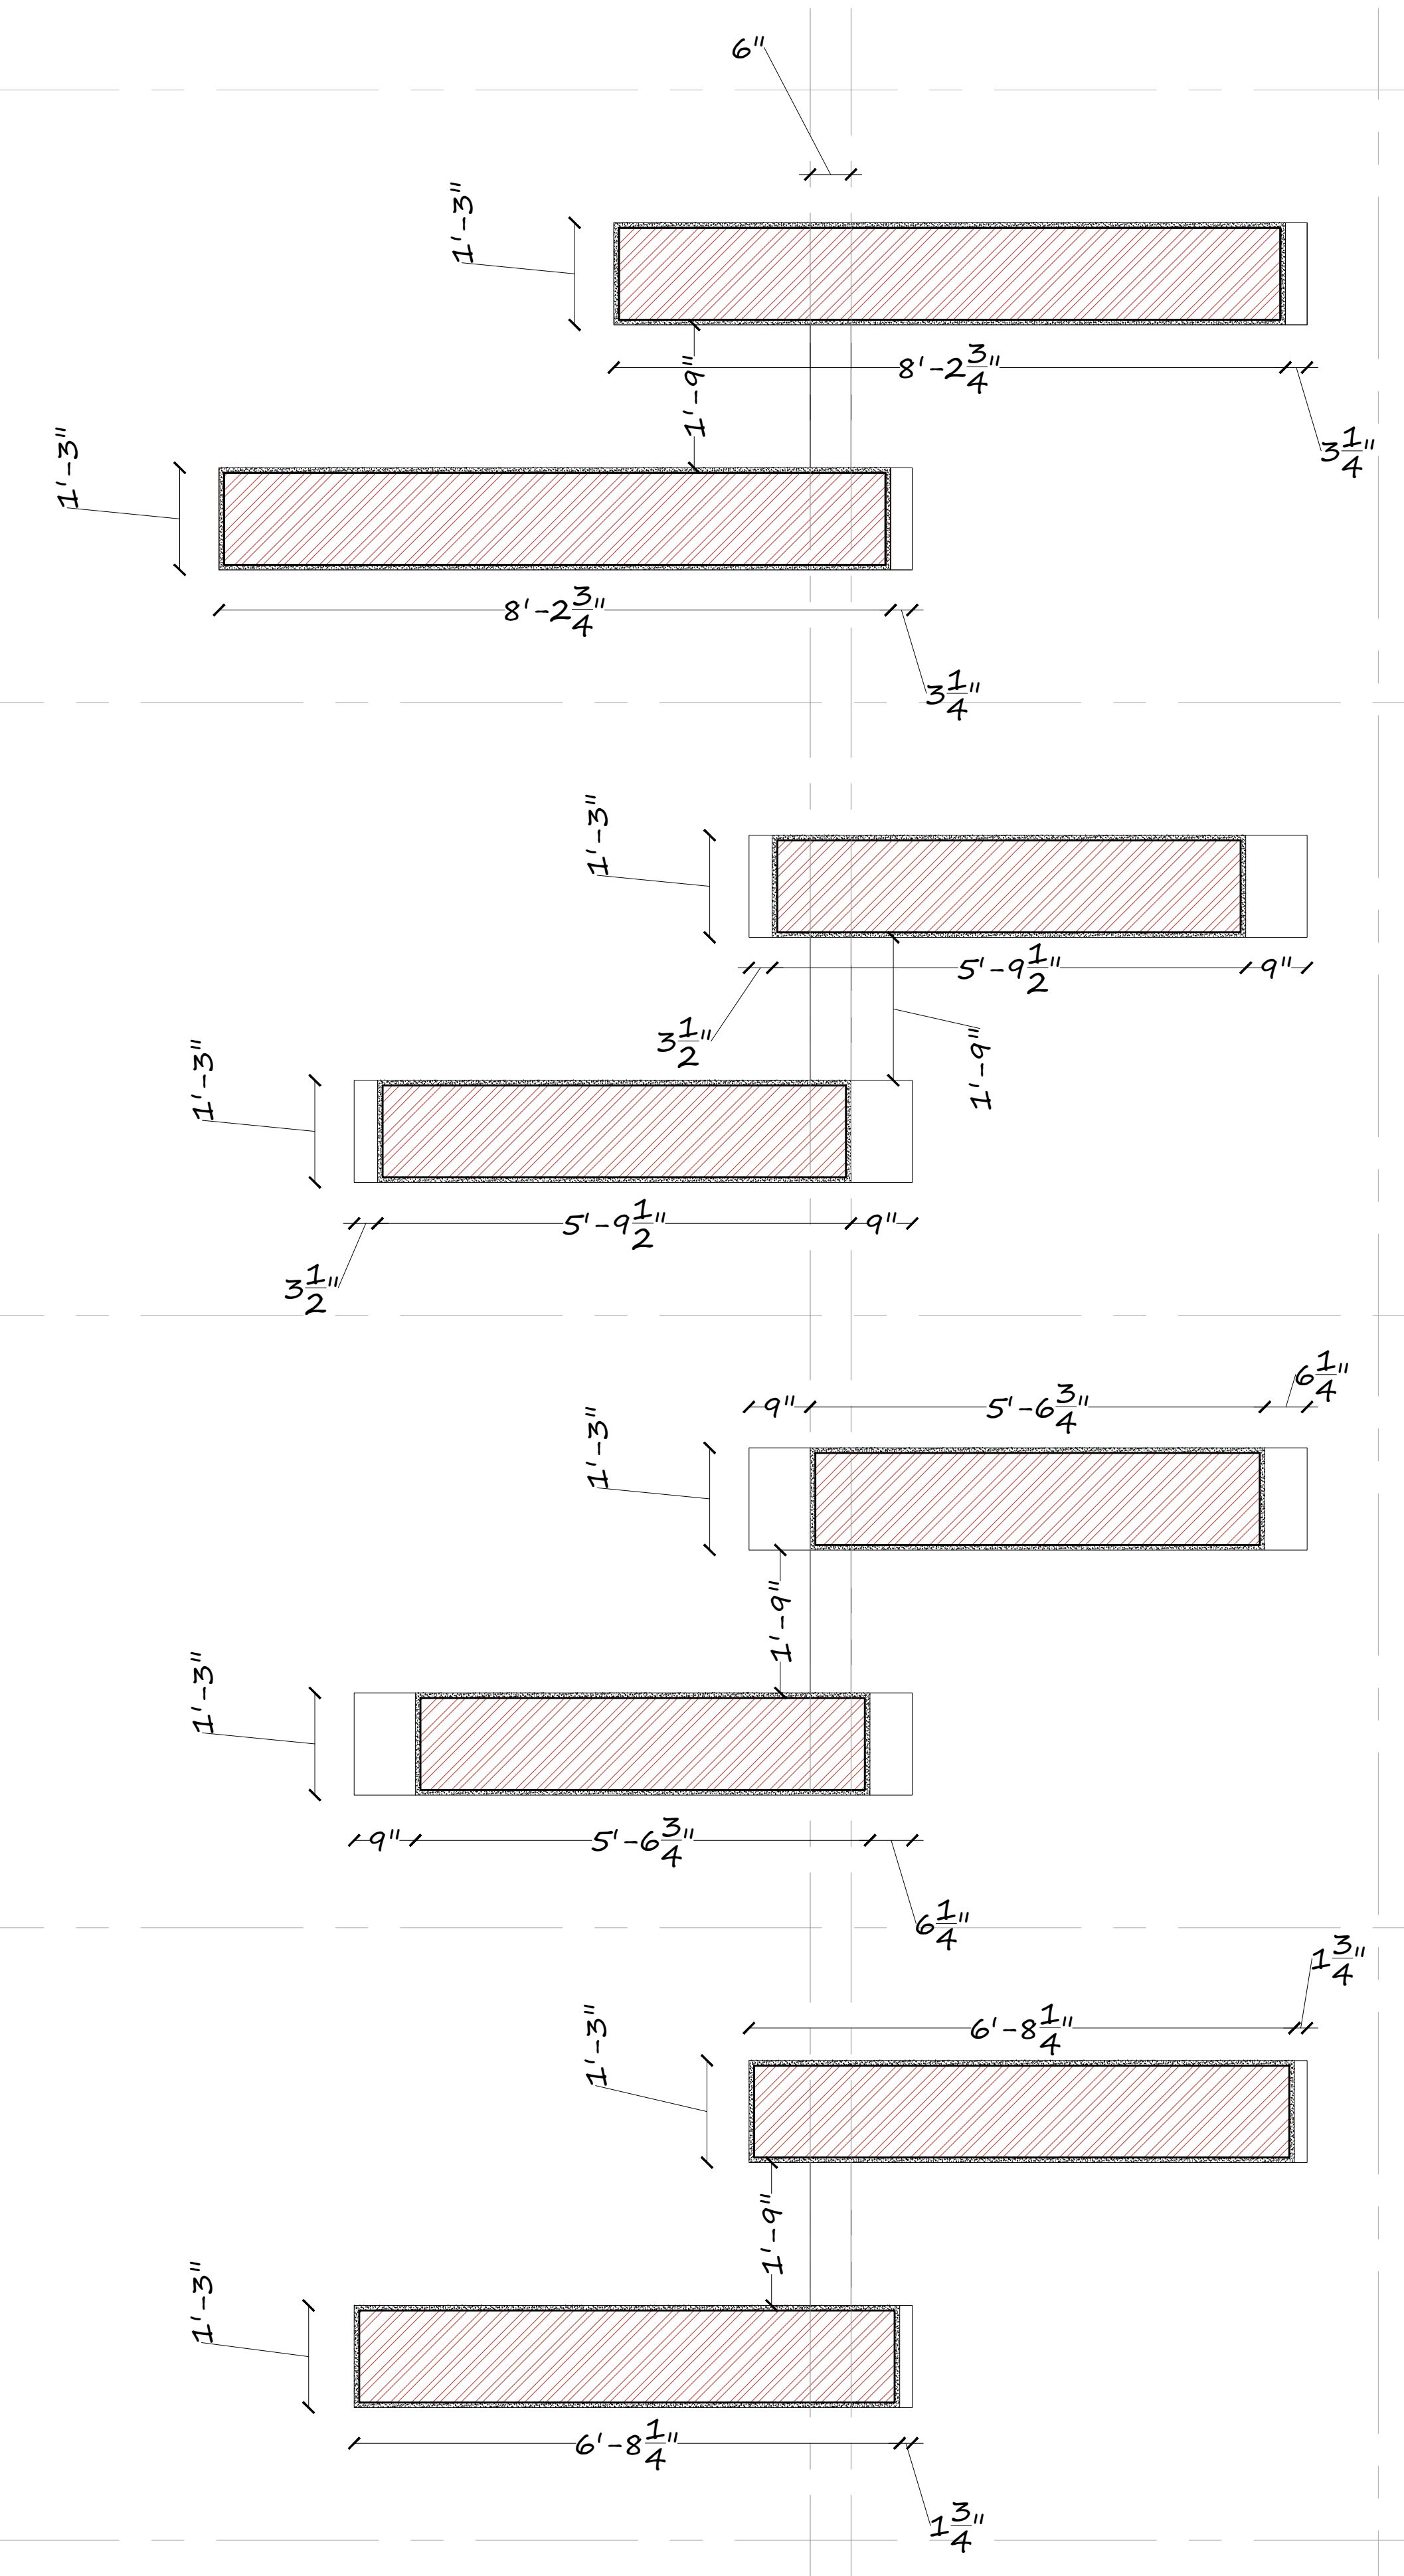

PLAN A

PLAN B

PLAN C

PLAN D

TREASURE TROVE VENUE

LOCATED AT
TIRUPPUR - TAMILNADU
[11°08'44.9"N 77°23'15.9"E]

Drg. Identification No.
EN20-D1-A

SCHEMATIC DETAIL
DIAGONAL WALL - PROTOTYPE


FOR BAR PROVISIONS

DESIGNED BY
DESIGN STRATEGIST [S1]

DATED : 22nd APRIL 2026

Represented as.	Description

REVISION - 'A'
[DATED - 28th MARCH 2026]
- Lintel Beam Proposed as per discussion

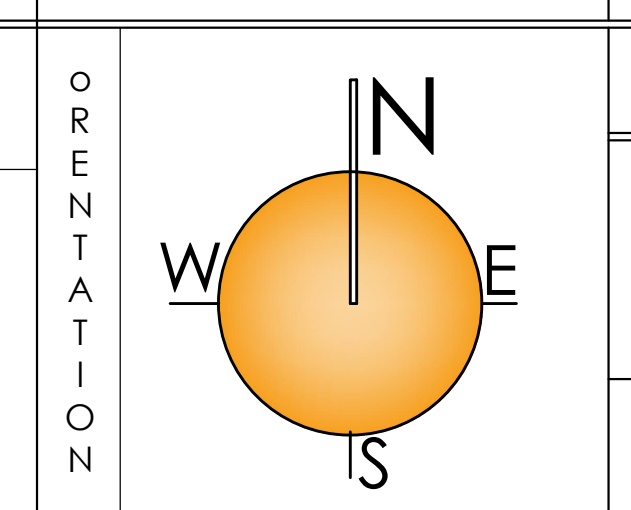

CTR INFRASTRUCTURE
96006 22928 | 6384-03-6384
infodesk@ctrinfrastructure.com
TIRUPPUR | COIMBATORE | BANGALORE
Established 1954

Architecture & planning
Design execution
Construction
Engineering
Promoting
Interior